기계제도 기능사 형식 연습용 · 가상 축 도면

교육용으로 직접 만든 도면입니다. 실제 기출 도면이 아니며, KS 적합성·제조 가능성을 검증하지 않았습니다.

정면도
제1각법

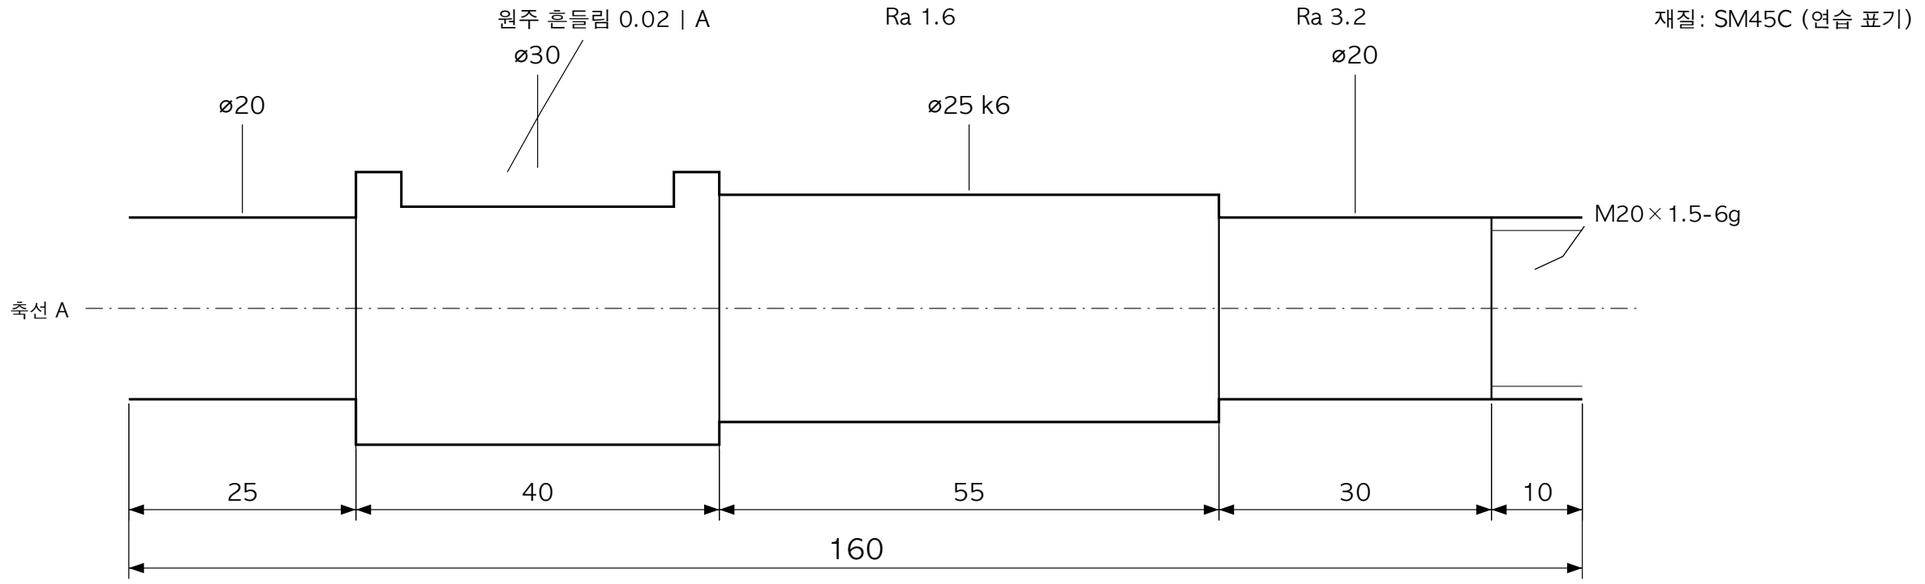

평면도

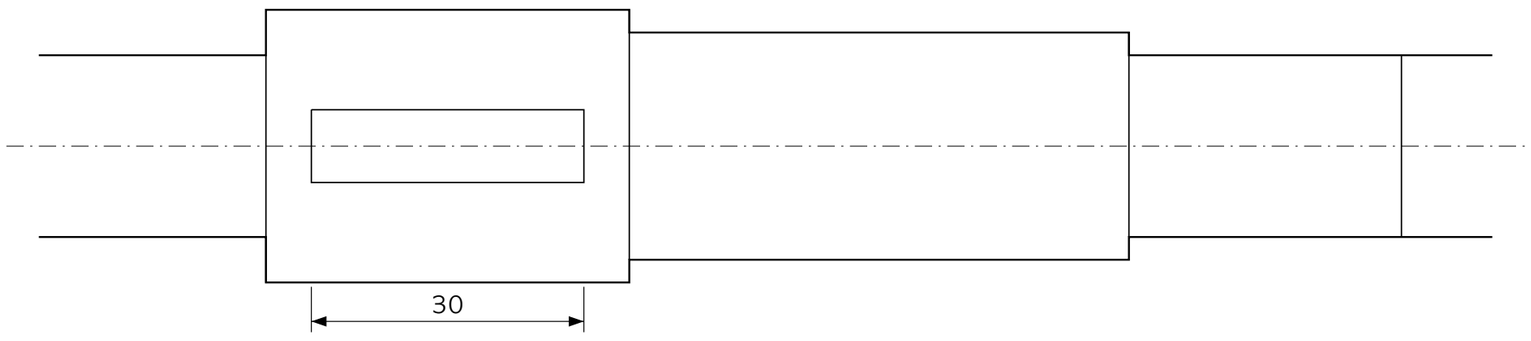

A - A 단면 (축 끝에서 봄)

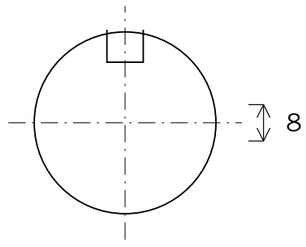

키홈 8×7, 길이 30
키홈 폭 8

재료·공차 기호는 연습용
미지정 치수는 판단하지 않음
베어링부: ø25 k6

도면명: 단차 축 (연습용)	투상법: 제1각법	축척: 1:1	연습
도면 번호: SHAFT-P-01	단위: mm	작성: 2026.11	1 / 1

이 도면은 교육용 가상 예제이며 실제 제작·검사 기준으로 사용할 수 없습니다.